

CONSTRUCTION PLANS

HILTON GARDEN INN

SITE IMPROVEMENTS


Section 15, Township 24 South, Range 37 East - Cape Canaveral, Brevard County, Florida

ALLEN
ENGINEERING, INC.

CIVIL ENGINEERS • SURVEYORS

106 Dixie Lane • Cocoa Beach, FL 32931 • Tel: 321-783-7443 • Fax: 321-783-5902 • www.AllenEng.net

Quality Performance Since 1963

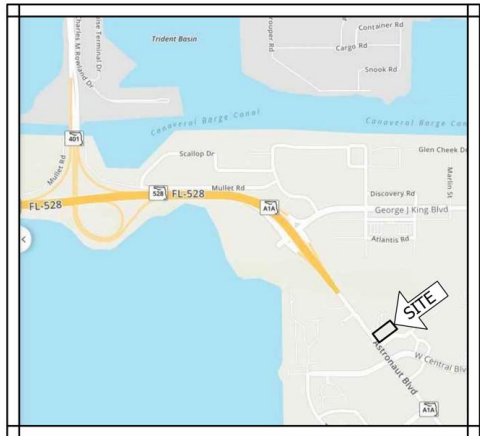

VICINITY MAP
NOT TO SCALE

PROJECT CONTACTS:

CLIENT:
McKibbin Hotel Group, Inc.
7 Old Roswell Street
Alpharetta, GA, 30009
Telephone: (770) 364-7384
c/o Jason Acree, Sr. Development Project Director
Email: jason.acree@ckkbbonplaces.com

ENGINEER:
Allen Engineering, Inc.
106 Dixie Lane
Cocoa Beach, FL 32931
Telephone: (321) 783-7443
Email: mallen@alleneng.net
Certificate of Authorization No. LB 266

SURVEYOR:
Bowman Consulting Group, Ltd., Inc.
301 S.E. Ocean Blvd., Suite 301
Stuart, FL 34994
Telephone: (772) 283-1413
Fax: (772) 283-7881
www.bowmanconsulting.com
Certificate NO. LB 8030

GENERAL STATEMENT:

THE PROPOSED PROJECT CONSISTS OF A NEW 6 STORY 156 ROOM HOTEL WITH POOL AND RESTAURANT. CONNECTION FOR DOMESTIC AND FIRE WILL BE MADE BY CONNECTING TO THE EXISTING 6" WATERMAIN ALONG THE EAST SIDE OF A1A. SEWER IS TO BE ROUTED TO THE REAR OF THE SITE TO THE EXISTING LINE ON SITE. STORMWATER TREATMENT IS PROVIDED ON SITE VIA AN INFILTRATION TRENCH SYSTEM THAT WILL OUTFALL TO FDOT'S ROW.

SITE LOCATION:

NE CORNER OF SR A1A AND IMPERIAL BLVD INTERSECTION IN CAPE CANAVERAL.

RECORD DESCRIPTION:

EXISTING CONDITIONS AND SURVEY INFORMATION IS FROM A BOWMAN CONSULTING GROUP, LTD., INC. ALTA / NSPS LAND TITLE BOUNDARY AND TOPOGRAPHIC SURVEY DATED DECEMBER 2, 2022.

LEGAL DESCRIPTION:

(PER BREVARD COUNTY PROPERTY APPRAISER WEBSITE)
PART OF SE 1/4 AS DESC IN ORB 3677 PG 4215
(PER TITLE COMMITMENT)
A PORTION OF SECTION 15, TOWNSHIP 24 SOUTH, RANGE 37 EAST, BREVARD COUNTY, FLORIDA, MORE PARTICULARLY DESCRIBED AS FOLLOWS:
COMMENCE AT A POINT ON THE EASTERLY RIGHT OF WAY LINE OF STATE ROAD #401 (A-1-A), A 100 FOOT RIGHT OF WAY, SAID POINT BEING 2448.56 FEET NORTH AS MEASURED AT RIGHT ANGLES TO THE SOUTH LINE OF SAID SECTION 15;
THENCE N 52 DEGREES 38' 50" E FOR A DISTANCE OF 486.00 FEET TO THE POINT OF BEGINNING;
THENCE S 37 DEGREES 21' 10" E FOR A DISTANCE OF 225.00 FEET;
THENCE S 52 DEGREES 38' 50" W FOR A DISTANCE OF 471.00 FEET TO A POINT OF CURVATURE OF A CURVE TO THE RIGHT HAVING A RADIUS OF 25.00 FEET;
THENCE NORTHWESTERLY ALONG THE ARC OF SAID CURVE THRU A CENTRAL ANGLE OF 90 DEGREES 00' 00" FOR A DISTANCE OF 39.27 FEET TO A POINT OF TANGENCY ON SAID EASTERLY RIGHT OF WAY LINE OF STATE ROAD # 401;
THENCE N 37 DEGREES 21' 10" W ALONG SAID EASTERLY RIGHT OF WAY LINE FOR A DISTANCE OF 125.00 FEET;
THENCE N 52 DEGREES 38' 50" E FOR A DISTANCE OF 200.00 FEET;
THENCE N 37 DEGREES 21' 10" W FOR A DISTANCE OF 75.00 FEET;
THENCE N 52 DEGREES 38' 50" E FOR A DISTANCE OF 286.00 FEET TO THE POINT OF BEGINNING.
TOGETHER WITH:
A PORTION OF SECTION 15, TOWNSHIP 24 SOUTH, RANGE 37 EAST, BREVARD COUNTY, FLORIDA, MORE PARTICULARLY DESCRIBED AS FOLLOWS:
BEGIN AT A POINT ON THE EASTERLY RIGHT OF WAY LINE OF STATE ROAD #401 (A-1-A), A 100.00 FOOT RIGHT OF WAY, SAID POINT BEING 2448.56 FEET NORTH OF AS MEASURED AT RIGHT ANGLES TO THE SOUTH LINE OF SAID SECTION 15;
THENCE NORTH 52 DEGREES 38' 50" EAST, FOR A DISTANCE OF 200.00 FEET;
THENCE SOUTH 37 DEGREES 21' 10" EAST, FOR A DISTANCE OF 75.00 FEET;
THENCE SOUTH 52 DEGREES 38' 50" WEST, FOR A DISTANCE OF 200.00 FEET TO A POINT ON THE EASTERLY RIGHT OF WAY LINE;
THENCE NORTH 37 DEGREES 21' 10" WEST ALONG SAID EASTERLY RIGHT OF WAY LINE, FOR A DISTANCE OF 75.00 FEET TO THE POINT OF BEGINNING.

INDEX OF DRAWINGS

DESCRIPTION	SHEET
CIVIL:	
COVER SHEET	C-000
GENERAL NOTES AND ABBREVIATIONS	C-001
EXISTING CONDITIONS AND DEMOLITION PLAN	C-100
SITE AND STRIPING PLAN	C-101
PAVING AND DRAINAGE PLAN	C-102
WATER AND SEWER PLAN	C-103
PAVING AND DRAINAGE DETAILS	C-501
PAVING AND DRAINAGE DETAILS	C-502
SANITARY SEWER DETAILS	C-503
WATER DETAILS	C-504
WATER TECHNICAL PROVISIONS	C-701
WATER TECHNICAL PROVISIONS	C-702
WATER TECHNICAL PROVISIONS	C-703
STORMWATER POLLUTION PREVENTION PLAN	C-704
TRUCK TURN PLAN	C-705
SURVEY: (BY OTHERS)	
ALTA / NSPS LAND TITLE BOUNDARY AND TOPOGRAPHIC SURVEY BY BOWMAN CONSULTING GROUP, LTD.	1-2 OF 2
LANDSCAPE: (BY OTHERS)	
HARDSCAPE PLAN	L-1 OF 3
LANDSCAPE PLAN	L-2 OF 3
LANDSCAPE SPECIFICATIONS	L-3 OF 3


Michael
S Allen

Digitally signed by Michael S
Allen
DN: c=US, o=ALLEN
ENGINEERING, INC.,
ou=A01410C000001768705787
FOOD080671, cn=Michael S Allen
Date: 2023.10.17 14:18:40
+0400

ISSUED FOR
REVIEW


NO.	DATE	REVISIONS	BY	CHK'D
1	10/2/23	PER CITY OF COCOA COMMENTS (10/2/23)	KS	D/W
2	8/15/23	PER FDOT COMMENTS (8/15/23)	RMB	D/W
3	7/24/23	PER FDOT COMMENTS (7/24/23)	KS	D/W
4	6/27/23	PER CITY OF CAPE CANAVERAL (6/01/23)	RMB	D/W



COPYRIGHT © 2023 ALLEN ENGINEERING, INC.
ALL RIGHTS RESERVED. NO PART OF THIS DOCUMENT MAY BE REPRODUCED OR TRANSMITTED IN ANY FORM OR BY ANY MEANS, ELECTRONIC OR MECHANICAL, WITHOUT PERMISSION IN WRITING FROM ALLEN ENGINEERING, INC.

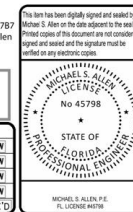

FOR: McKIBBIN HOTEL GROUP, INC.		DATE: 2-01-23
HILTON GARDEN INN CAPE CANAVERAL, BREVARD COUNTY, FLORIDA		SCALE:
COVER SHEET		N.T.S.
ALLEN ENGINEERING, INC. CIVIL ENGINEERS • SURVEYORS FLORIDA CERTIFICATE OF AUTHORIZATION NO. LB 266 106 DIXIE LANE, COCOA BEACH, FLORIDA 32931 TELEPHONE: (321) 783-7443 • FAX: (321) 783-5902 WEBSITE: www.alleneng.net • EMAIL: info@alleneng.net		JOB NO. 220028
		DRAWN: RMB
		SHT. NO. C-000



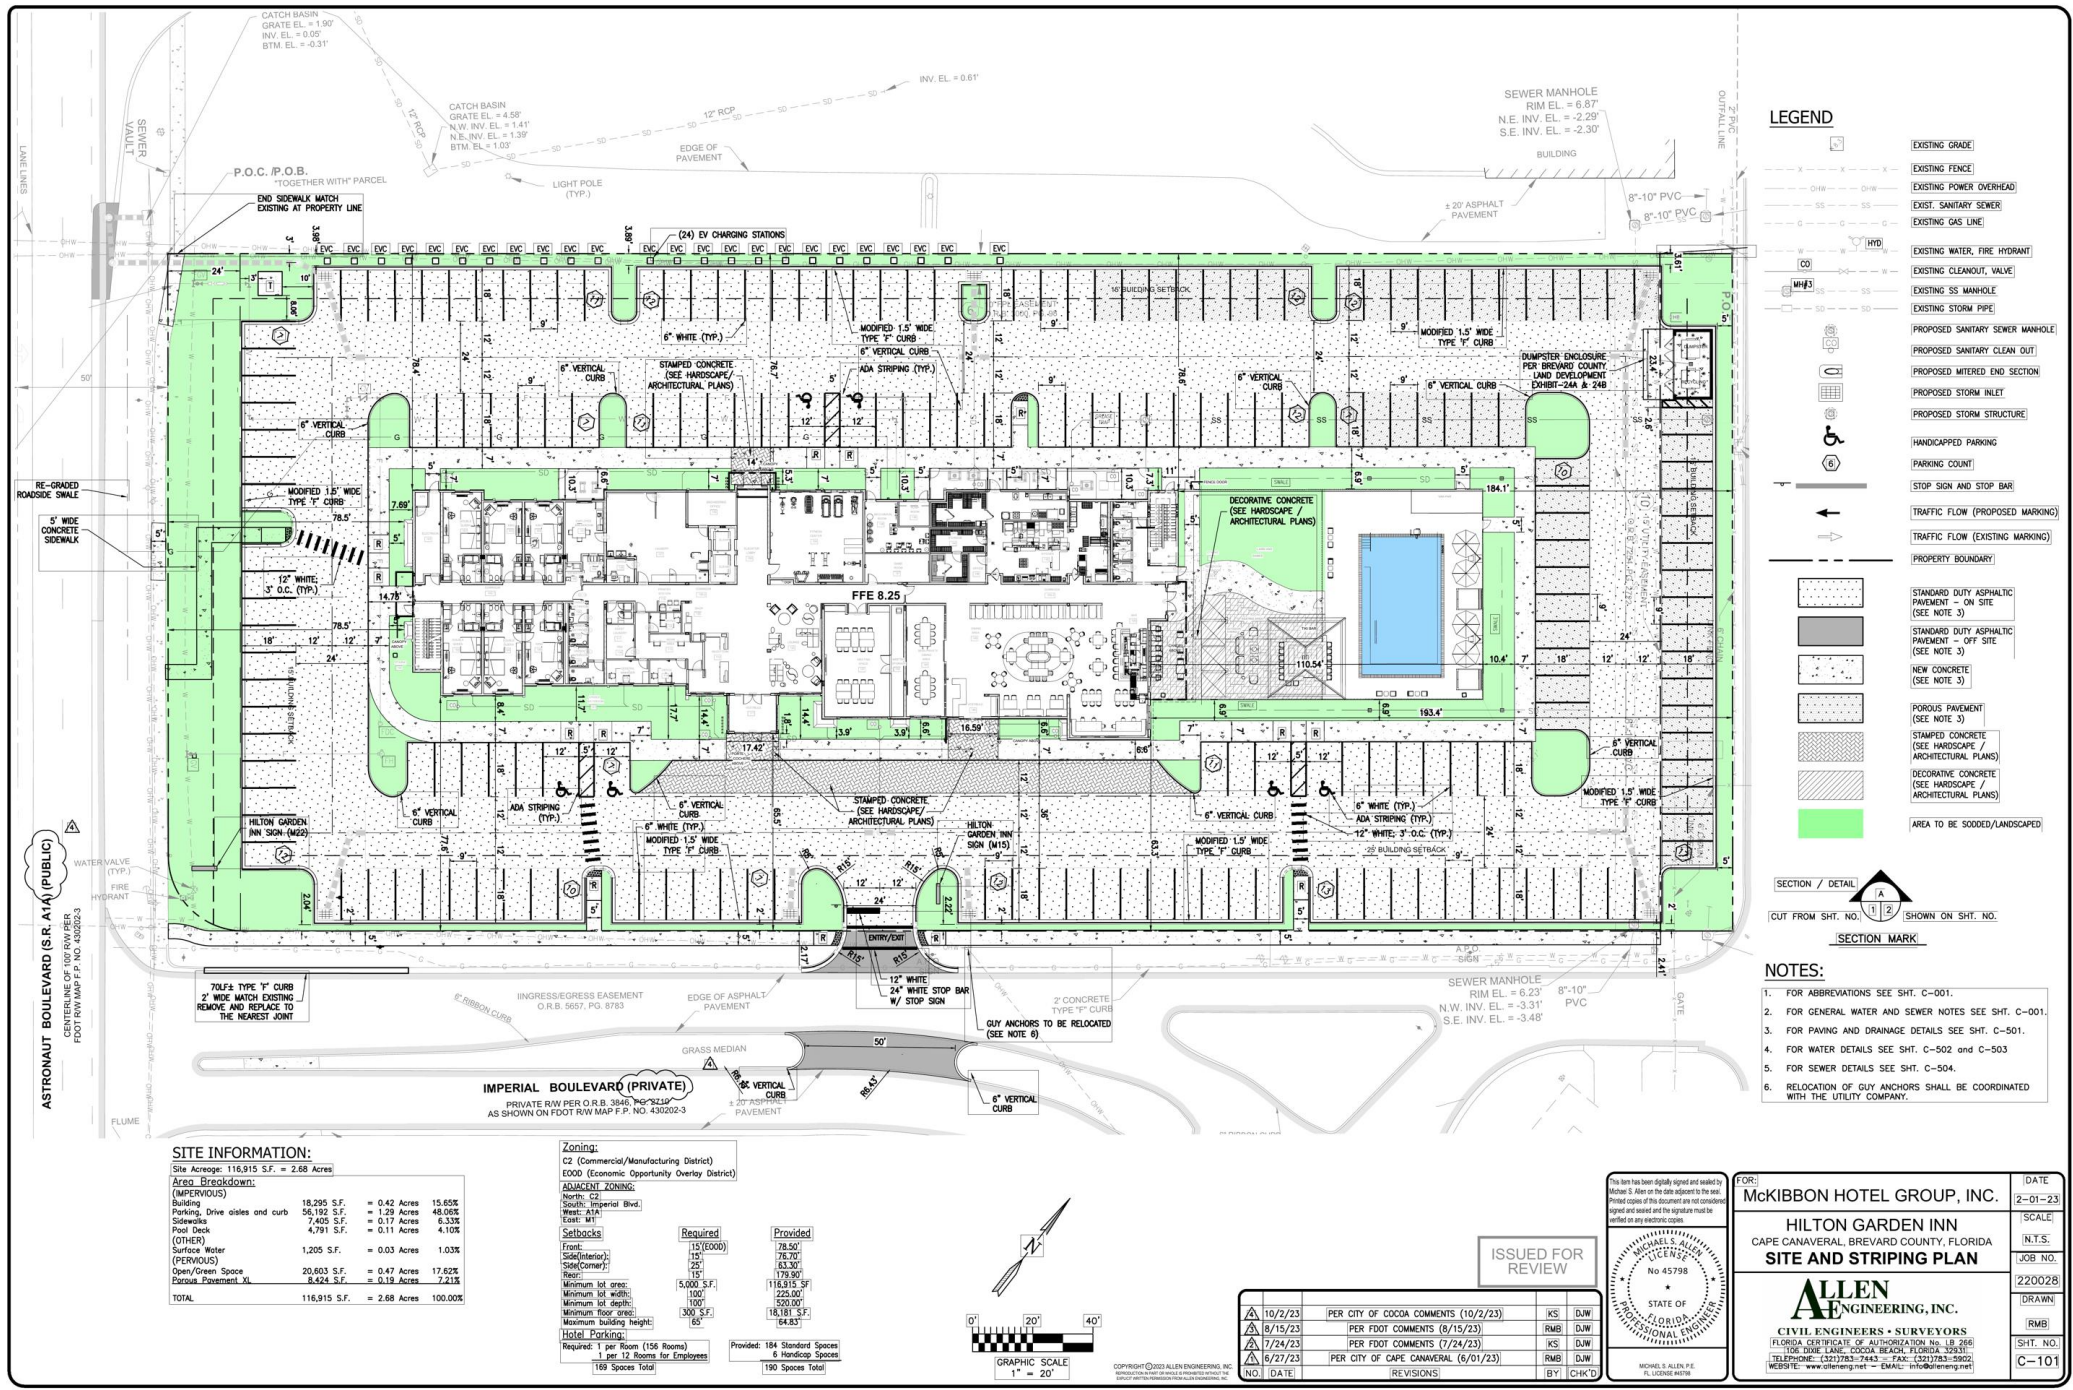

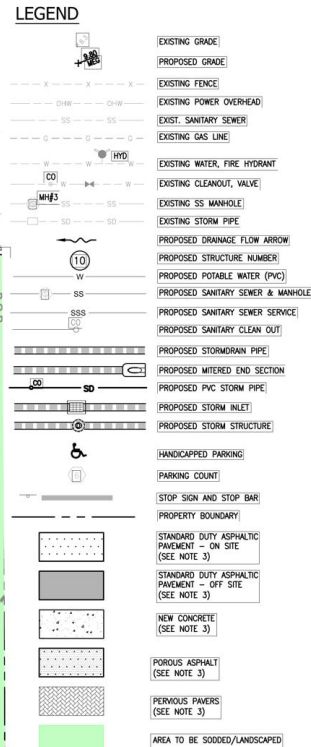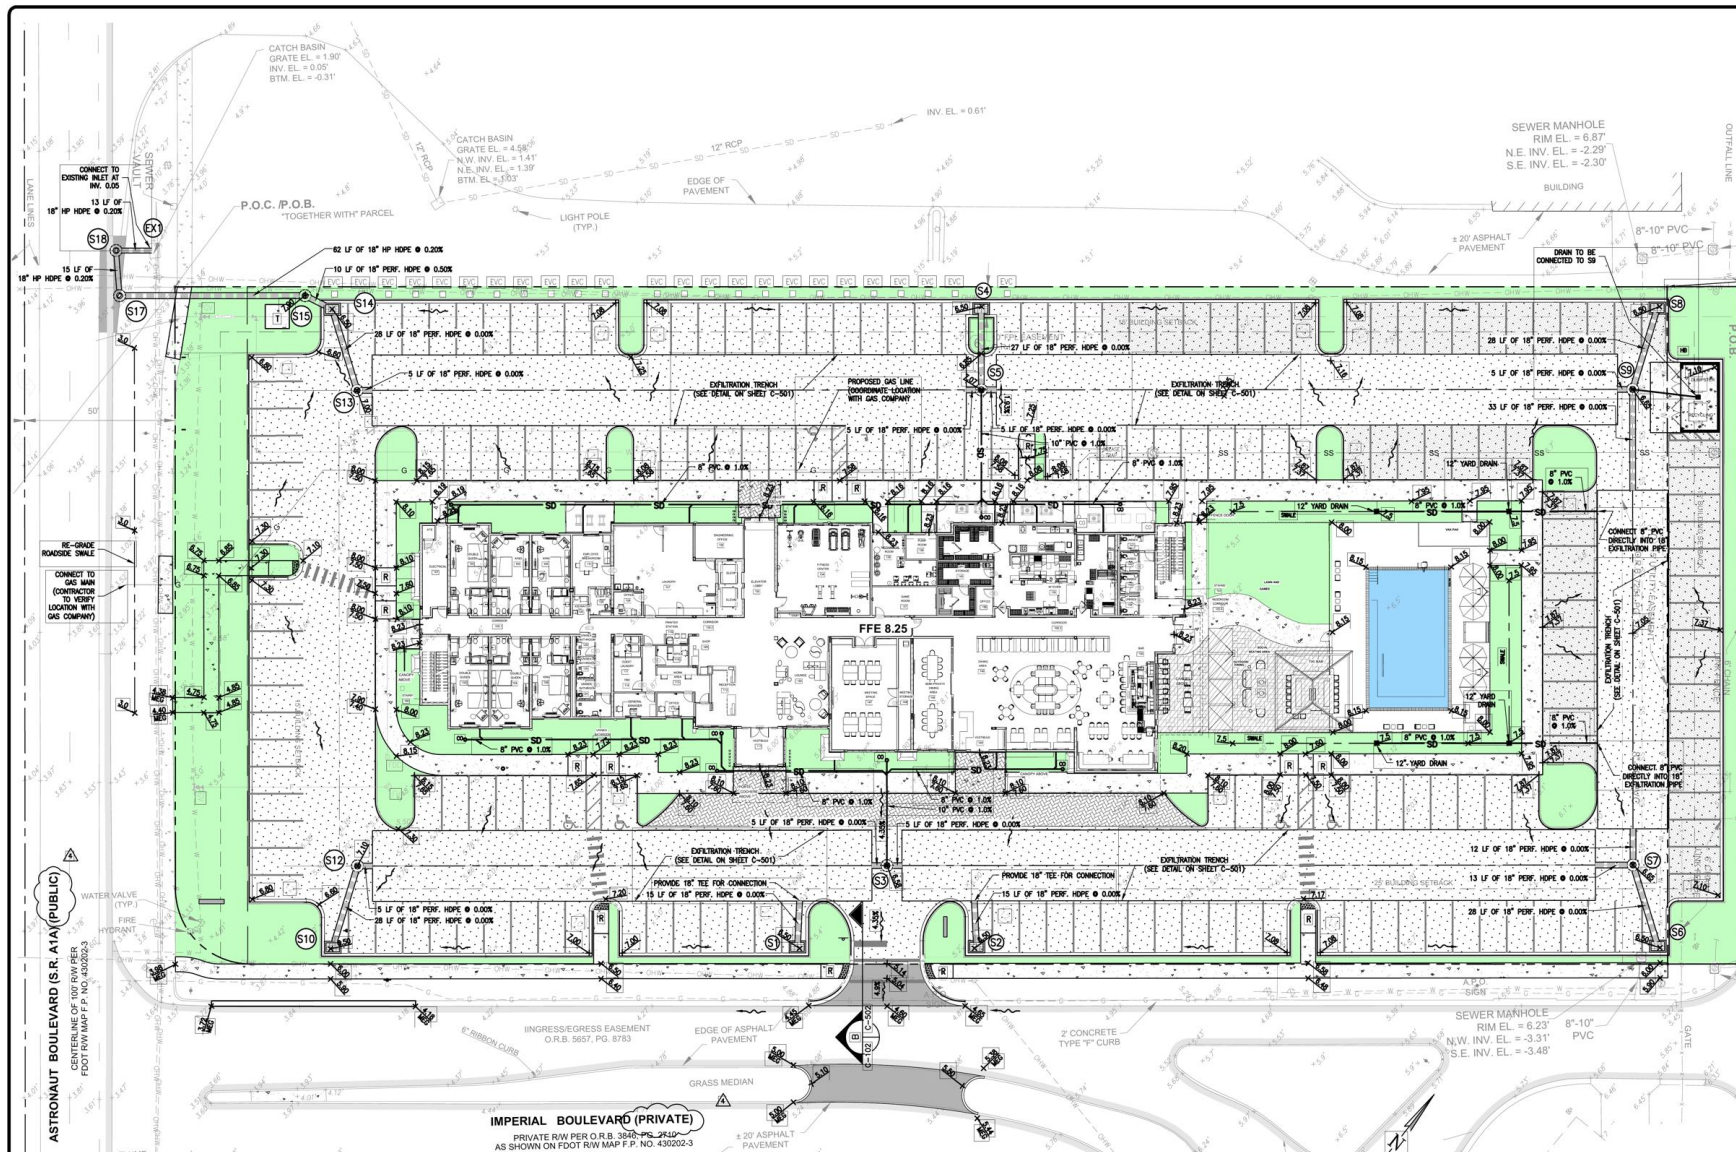

- NOTES:**
- FOR ABBREVIATIONS SEE SHT. C-001.
 - FOR GENERAL WATER AND SEWER NOTES SEE SHT. C-001.
 - FOR PAVING AND DRAINAGE DETAILS SEE SHT. C-501.
 - FOR WATER DETAILS SEE SHT. C-502 AND C-503.
 - FOR SEWER DETAILS SEE SHT. C-504.
 - SIDEWALKS TO BE CONSTRUCTED TO THE CITY OF CAPE CANAVERAL STANDARDS.
 - 18" PERFORATED (PERF.) HOPE PIPE TO HAVE ROCK ENVELOPE PER "ROCK ENVELOPE DETAIL" ON SHEET C-501.
 - OVER EXCAVATE 10' BEYOND AND 5' BELOW EXFILTRATION TRENCH. REMOVE UNDESIRABLE SOILS. BACKFILL WITH CLEAN SANDS HAVING LESS THAN 10% FINES AND A PERMEABILITY RATE GREATER THAN 15 IN/HR.


STRUCTURE TABLE				STRUCTURE DETAILS			
STRUCTURE ID	DESCRIPTION	NORTHING	EASTING	TOP/GRATE	IN	OUT	DETAIL
EX1	EX INLET	1477675.109	780358.182	TOP/GRATE = 1.90	INV IN = 0.05 (D)	INV OUT = 0.05 (D)	
S1	TYPE E	1477624.299	780666.792	TOP/GRATE = 6.50	INV IN = 4.00 (NW)	INV OUT = 4.00 (NW)	
S2	TYPE E	1477660.083	780715.540	TOP/GRATE = 6.50	INV IN = 4.00 (NW)	INV OUT = 4.00 (NW)	
S3	DMH 4' DIA.	1477663.852	780675.723	TOP/GRATE = 6.58	INV IN = 4.50 (NW)	INV OUT = 4.00 (NW)	
S4	TYPE E	1477629.354	780686.256	TOP/GRATE = 6.50	INV IN = 4.00 (D)	INV OUT = 4.00 (D)	

STRUCTURE TABLE				STRUCTURE DETAILS			
STRUCTURE ID	DESCRIPTION	NORTHING	EASTING	TOP/GRATE	IN	OUT	DETAIL
S5	DMH 4' DIA.	1477687.694	780603.201	TOP/GRATE = 7.07	INV IN = 4.00 (NW)	INV OUT = 4.00 (D)	
S6	TYPE E	1477800.506	780895.063	TOP/GRATE = 6.50	INV IN = 4.00 (NW)	INV OUT = 4.00 (NW)	
S7	DMH 4' DIA.	1477816.647	780871.063	TOP/GRATE = 6.65	INV IN = 4.00 (D)	INV OUT = 4.00 (NW)	
S8	TYPE E	1477968.262	780763.844	TOP/GRATE = 6.50	INV IN = 4.00 (D)	INV OUT = 4.00 (D)	
S9	DMH 4' DIA.	1477941.081	780773.730	TOP/GRATE = 6.65	INV IN = 4.00 (N)	INV OUT = 4.00 (D)	


STRUCTURE TABLE				STRUCTURE DETAILS			
STRUCTURE ID	DESCRIPTION	NORTHING	EASTING	TOP/GRATE	IN	OUT	DETAIL
S10	TYPE E	1477938.235	780546.980	TOP/GRATE = 6.50	INV IN = 4.00 (N)	INV OUT = 4.00 (N)	
S12	DMH 4' DIA.	1477955.416	780537.095	TOP/GRATE = 7.10	INV IN = 4.00 (D)	INV OUT = 4.00 (D)	
S13	DMH 4' DIA.	1477979.851	780439.762	TOP/GRATE = 7.00	INV IN = 4.00 (NW)	INV OUT = 4.00 (NW)	
S14	TYPE E	1477968.035	780416.626	TOP/GRATE = 6.50	INV IN = 4.00 (D)	INV OUT = 4.00 (N)	

STRUCTURE TABLE				STRUCTURE DETAILS			
STRUCTURE ID	DESCRIPTION	NORTHING	EASTING	TOP/GRATE	IN	OUT	DETAIL
S15	DMH 5' DIA.	1477684.022	780406.777	TOP/GRATE = 6.50	INV IN = 3.95 (D)	INV OUT = 3.93 (NW)	
S17	DMH 4' DIA.	1477656.064	780358.187	TOP/GRATE = 3.62	INV IN = 0.11 (D)	INV OUT = 0.11 (D)	
S18	DMH 4' DIA.	1477687.161	780346.020	TOP/GRATE = 3.85	INV IN = 0.08 (D)	INV OUT = 0.08 (D)	

NO.	DATE	REVISIONS	BY	CHK'D
1	10/2/23	PER CITY OF COCOA COMMENTS (10/2/23)	KS	D/W
2	8/15/23	PER FOOT COMMENTS (8/15/23)	RMB	D/W
3	7/24/23	PER FOOT COMMENTS (7/24/23)	KS	D/W
4	6/27/23	PER CITY OF CAPE CANAVERAL (6/01/23)	RMB	D/W

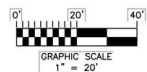

ISSUED FOR REVIEW

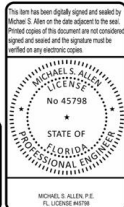

FOR: **MCKIBBON HOTEL GROUP, INC.**

HILTON GARDEN INN
CAPE CANAVERAL, BREVARD COUNTY, FLORIDA
PAVING AND DRAINAGE PLAN

ALLEN ENGINEERING, INC.
CIVIL ENGINEERS • SURVEYORS
FLORIDA CERTIFICATE OF AUTHORIZATION NO. LB 266
100 DORE LANE, COCOA BEACH, FLORIDA 32931
TELEPHONE: (321)783-7443 • FAX: (321)783-5862
WEBSITE: www.alleneng.net • EMAIL: info@alleneng.net

DATE: 2-01-23

SCALE: N.T.S.

JOB NO.: 220028

DRAWN: RMB

SHT. NO.: C-102